

[İŞVEREN ADI]

ERA EVİ

MİMARİ KONSEPT PROJE

KONUT PROJESİ

(11.11.2026)

İÇİNDEKİLER

- PROJE BİLGİLERİ
- VAZİYET PLANI
- SİTE GÖRSELİ
- A BLOK: GÖRSEL VE KAT PLANLARI
- B BLOK: GÖRSEL VE KAT PLANLARI
- C BLOK: GÖRSEL VE KAT PLANLARI
- D BLOK: GÖRSEL VE KAT PLANLARI
- ALAN TABLOSU
- ATMOSFER ESKİZİ

PROJE ALANI: UYDU GÖRÜNTÜSÜ / KONUM HARİTASI

IFC tarafından eklenecek (oran 1.29 : 1, 290 × 225 mm)

PROJE BİLGİLERİ

LOKASYON: Beykoz / İstanbul
MAHALLE: [DOLDURULACAK]
ADA / PARSEL: 1366 ADA 45 PARSEL
SOKAK: Güller Sokak, Odak Çıkmazı Sokak
ARSA ALANI: [DOLDURULACAK] m²
BLOK ADEDİ: 4 BLOK (A, B, C, D)
BAĞIMSIZ BÖLÜM: [DOLDURULACAK]
TOPLAM KAPALI ALAN: 2361.18 m²

[DOLDURULACAK: Proje tanıtım / konsept metni. İşveren ve konsept fikirleri verildiğinde, ofisin önceki sunumlarındaki (Yavuzselim) metinle aynı dil, ton ve üslupta 3–4 paragraf olarak yazılacak.]

[Paragraf 2: yerleşim ve topoğrafya kararları.]

[Paragraf 3: blokların kurgusu, açık alanlar ve peyzaj.]

[Paragraf 4: malzeme ve mimari dil.]

VAZİYET PLANI

ADA 1366 · PARSEL 45



LEJANT

- Yapı (çatı planı)
- Zemin kat izi / teras
- Çim / doğal eğim
- Yaya yolu / sert zemin
- Araç yolu / rampa / açık otopark
- Şev taşı / kademeli set
- Yol / kaldırım (parsel dışı)
- Set / istinat / bahçe duvarı
- Parsel sınırı
- Bina girişi
- Kot (m)

BLOKLAR

A BLOK	1BK+Z+1N = 3 KAT ±0.00 = 172.95 (SUBASMAN +1.20 = 174.15)
B BLOK	2BK+Z = 3 KAT ±0.00 = 174.15
C BLOK	1BK+Z = 2 KAT ±0.00 = 174.36
D BLOK	1BK+Z+1N = 3 KAT ±0.00 = 167.25

ÖLÇEK 1/500

0 5 10 15 20 25 m

VAZİYET PLANI





A BLOK 1BK+Z+1N = 3 KAT ±0.00 = 172.95
TOPLAM KAPALI ALAN : 677.04 m²

K

ÖLÇEK 1/200
0 2 4 6 8 10 m



A BLOK · 1. BODRUM KAT PLANI

KOT -2.80 (170.15)

NET ALAN TOPLAMI : 327.40 m²

BRÜT ALAN : 362.00 m²

No	Mahal	Net alan (m²)
1	BANYO	4.30
2	KORİDOR	8.90
3	ŞOK DUŞ	2.20



A BLOK · ZEMİN KAT PLANI


KOT +1.20 (174.15)

NET ALAN TOPLAMI : 150.40 m²

AÇIK ALAN (TERAS/BALKON/BAHÇE) : 190.00 m²

BRÜT ALAN : 170.00 m²

No	Mahal	Net alan (m²)
1	TEMİZLİK ODASI	2.40
2	MERDİVEN	4.00

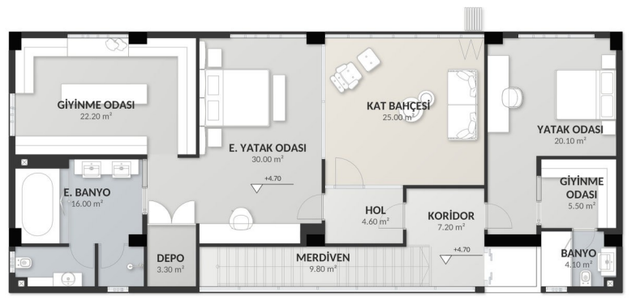

A BLOK · 1. KAT PLANI

KOT +4.70 (177.65)

NET ALAN TOPLAMI : 122.80 m²

AÇIK ALAN (TERAS/BALKON/BAHÇE) : 25.00 m²

BRÜT ALAN : 145.04 m²

TOPLAM KAPALI ALAN : 677.04 m²



K

ÖLÇEK 1/100

0 1 2 3 4 5 m

A BLOK · 1. BODRUM KAT PLANI

KOT -2.80 (170.15)

NET ALAN TOPLAMI : 327.40 m²

BRÜT ALAN : 362.00 m²

A BLOK · ZEMİN KAT PLANI

KOT +1.20 (174.15)



K

ÖLÇEK 1/100

0 1 2 3 4 5 m


A BLOK · ZEMİN KAT PLANI

KOT +1.20 (174.15)

NET ALAN TOPLAMI : 150.40 m²

AÇIK ALAN (TERAS/BALKON/BAHÇE) : 190.00 m²

BRÜT ALAN : 170.00 m²

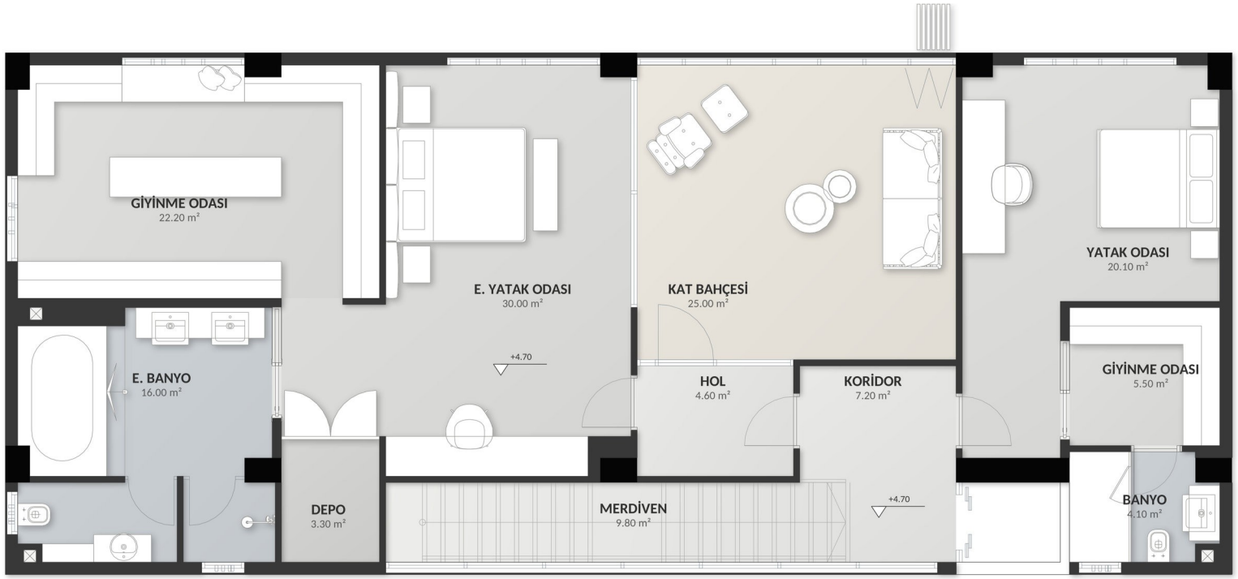

ÖLÇEK 1/100
0 1 2 3 4 5 m


A BLOK · 1. KAT PLANI
KOT +4.70 (177.65)
NET ALAN TOPLAMI : 122.80 m²
AÇIK ALAN (TERAS/BALKON/BAHÇE) : 25.00 m²
BRÜT ALAN : 145.04 m²



B BLOK 2BK+Z = 3 KAT ±0.00 = 174.15
TOPLAM KAPALI ALAN : 954.12 m²

K


ÖLÇEK 1/250
0 2 4 6 8 10 m

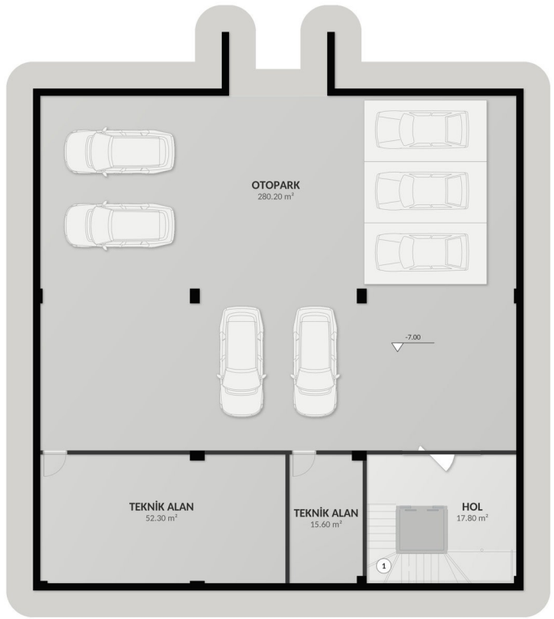

B BLOK · 2. BODRUM KAT PLANI

KOT -7.00 (167.15)
NET ALAN TOPLAMI : 376.00 m²
BRÜT ALAN : 409.00 m²


No	Mahal	Net alan (m²)
1	MERDİVEN	10.10

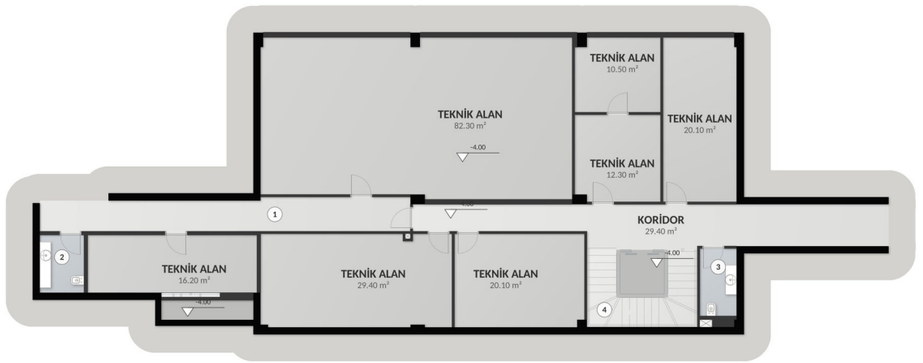

B BLOK · 1. BODRUM KAT PLANI

KOT -4.00 (170.15)
NET ALAN TOPLAMI : 258.50 m²
BRÜT ALAN : 301.68 m²

No	Mahal	Net alan (m²)
1	KORİDOR	19.80
2	WC	4.20
3	WC	4.10
4	MERDİVEN	10.10

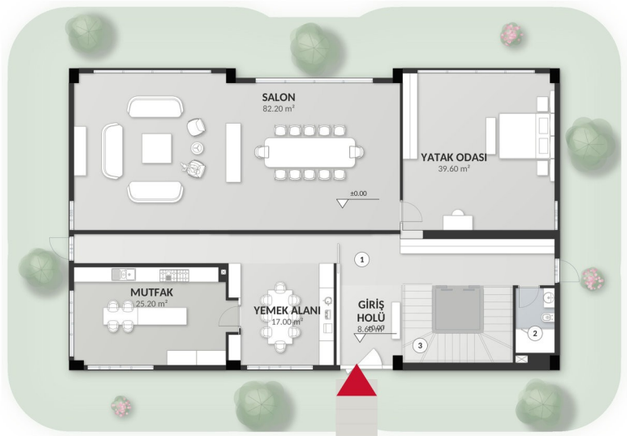

B BLOK · ZEMİN KAT PLANI

KOT ±0.00 (174.15)
NET ALAN TOPLAMI : 217.20 m²
BRÜT ALAN : 243.44 m²


No	Mahal	Net alan (m²)
1	KORİDOR	30.30
2	BANYO	4.20
3	MERDİVEN	10.10

TOPLAM KAPALI ALAN : 954.12 m²

B BLOK · 2. BODRUM KAT PLANI

KOT -7.00 (167.15)

K

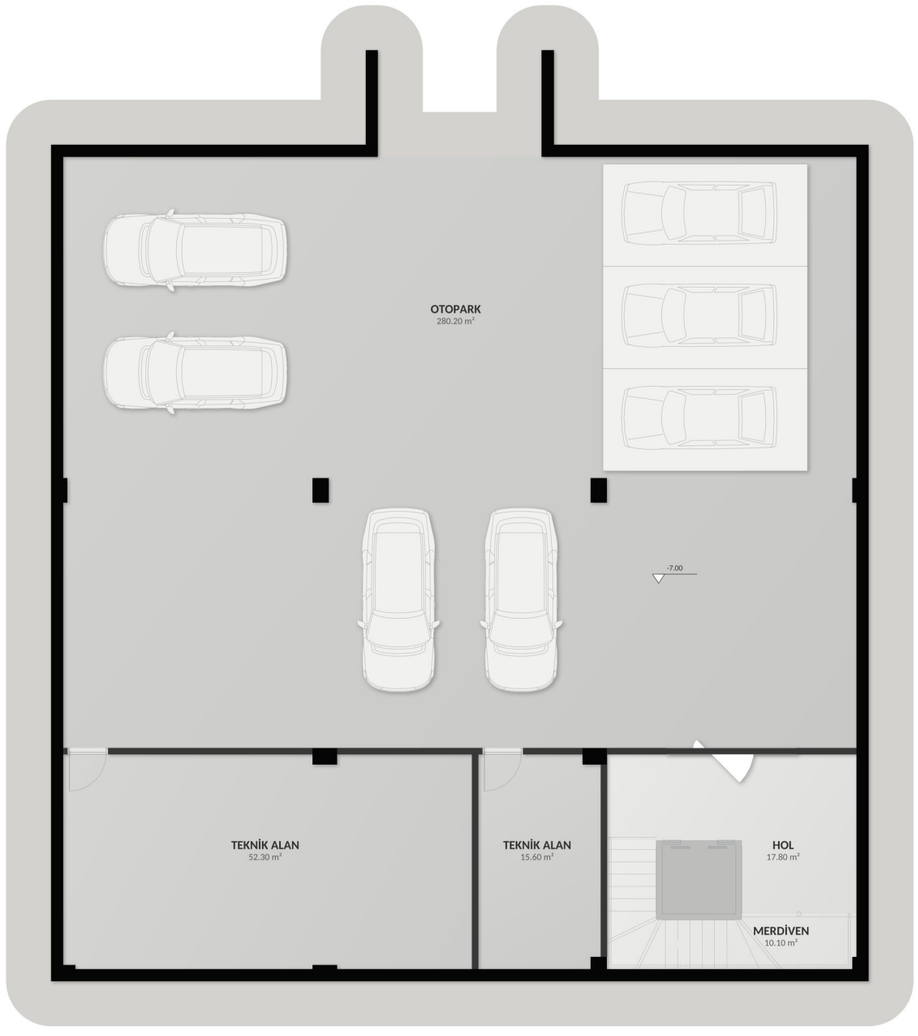

ÖLÇEK 1/150

0 2 4 6 8 10 m

B BLOK · 2. BODRUM KAT PLANI

KOT -7.00 (167.15)

NET ALAN TOPLAMI : 376.00 m²

BRÜT ALAN : 409.00 m²

B BLOK · 1. BODRUM KAT PLANI

KOT -4.00 (170.15)

K

No	Mahal	Net alan (m²)
1	MERDİVEN	10.10



ÖLÇEK 1/150

0 2 4 6 8 10 m


B BLOK · 1. BODRUM KAT PLANI

KOT -4.00 (170.15)

NET ALAN TOPLAMI : 258.50 m²

BRÜT ALAN : 301.68 m²

K

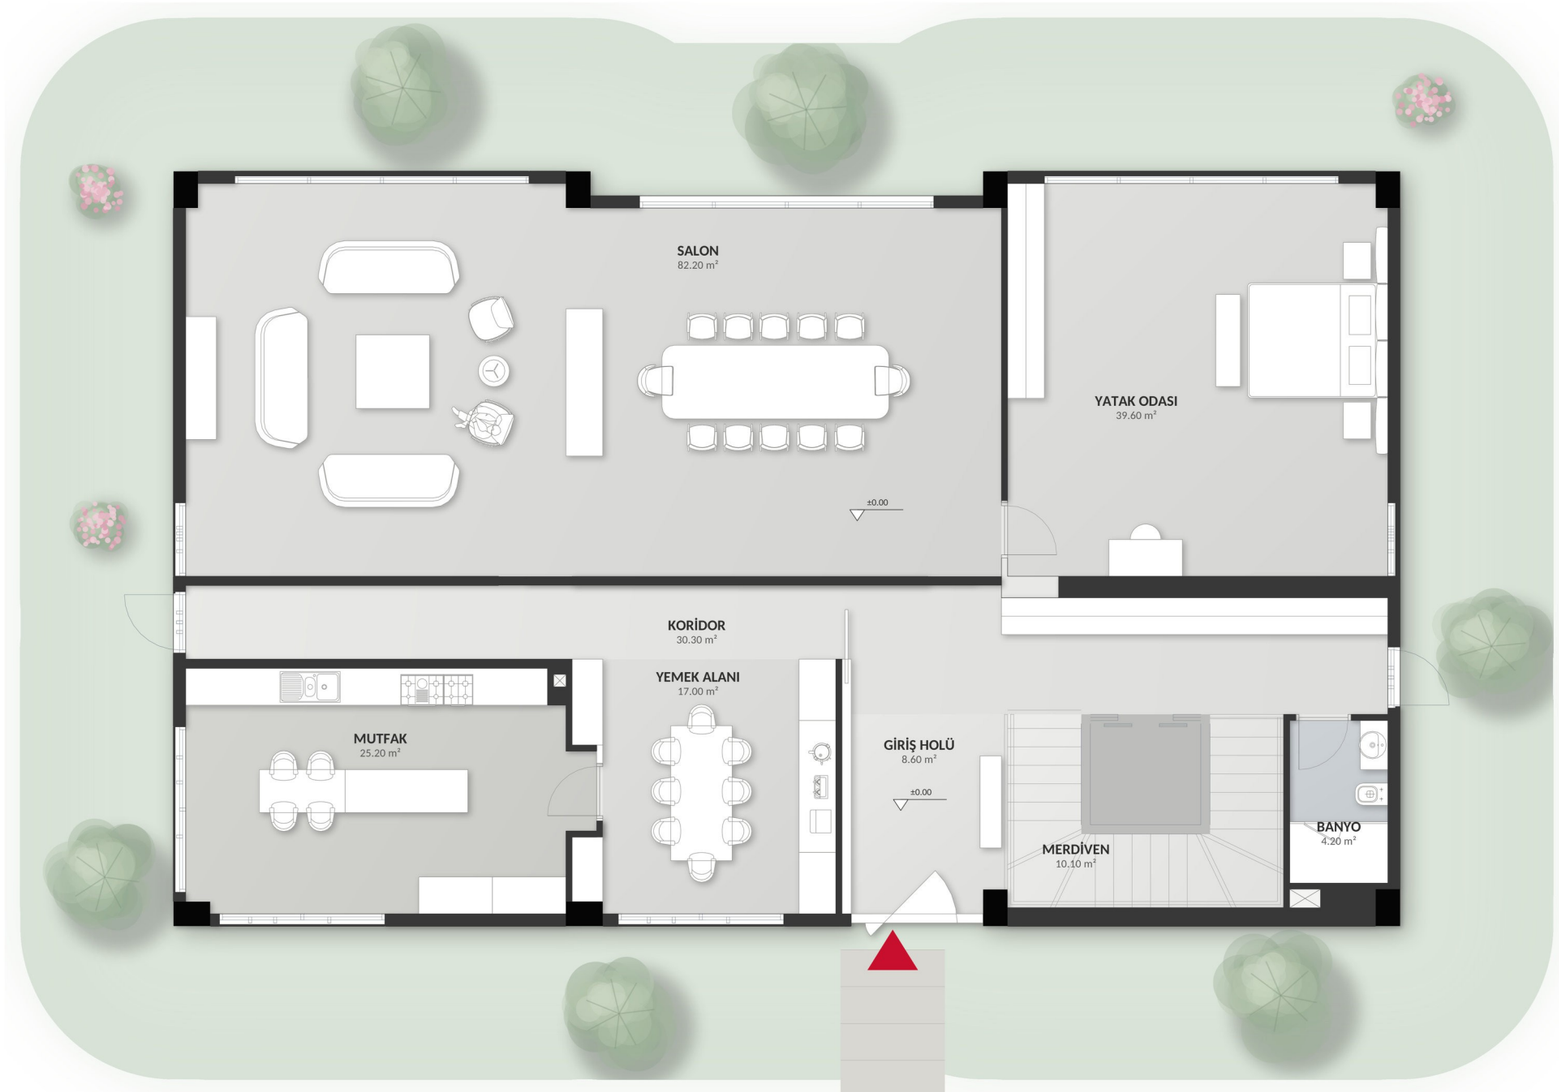

ÖLÇEK 1/100

0 1 2 3 4 5 m

B BLOK · ZEMİN KAT PLANI

KOT ±0.00 (174.15)

NET ALAN TOPLAMI : 217.20 m²

BRÜT ALAN : 243.44 m²

GÖRSEL: C BLOK

IFC tarafından eklenecek (oran 2.17 : 1, 420 × 193.5 mm)

C BLOK 1BK+Z = 2 KAT ±0.00 = 174.36
TOPLAM KAPALI ALAN : 270.00 m²

K

ÖLÇEK 1/150
0 1 2 3 4 5 m



C BLOK · 1. BODRUM KAT PLANI

KOT -4.00 (170.36)
NET ALAN TOPLAMI : 117.80 m²
BRÜT ALAN : 135.00 m²

No	Mahal	Net alan (m²)
1	MERDİVEN	6.20



C BLOK · ZEMİN KAT PLANI

KOT ±0.00 (174.36)
NET ALAN TOPLAMI : 107.10 m²
AÇIK ALAN (TERAS/BALKON/BAHÇE) : 13.60 m²
BRÜT ALAN : 135.00 m²

TOPLAM KAPALI ALAN : 270.00 m²

K



ÖLÇEK 1/100

0 1 2 3 4 5 m

C BLOK · 1. BODRUM KAT PLANI

KOT -4.00 (170.36)

NET ALAN TOPLAMI : 117.80 m²

BRÜT ALAN : 135.00 m²

K



ÖLÇEK 1/100

0 1 2 3 4 5 m

C BLOK · ZEMİN KAT PLANI


KOT ±0.00 (174.36)
NET ALAN TOPLAMI : 107.10 m²
AÇIK ALAN (TERAS/BALKON/BAHÇE) : 13.60 m²
BRÜT ALAN : 135.00 m²



D BLOK 1BK+Z+1N = 3 KAT ±0.00 = 167.25
TOPLAM KAPALI ALAN : 460.02 m²

K

ÖLÇEK 1/150
0 1 2 3 4 5 m

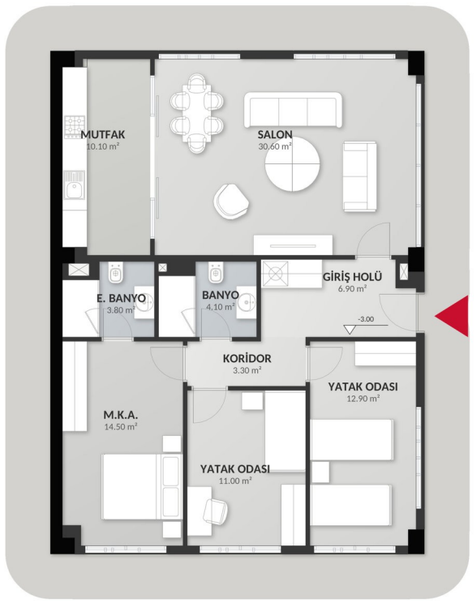

D BLOK · 1. BODRUM KAT PLANI

KOT -3.00 (164.25)

NET ALAN TOPLAMI : 97.20 m²

BRÜT ALAN : 112.54 m²




D BLOK · ZEMİN KAT PLANI

KOT ±0.00 (167.25)

NET ALAN TOPLAMI : 191.40 m²

BRÜT ALAN : 217.71 m²

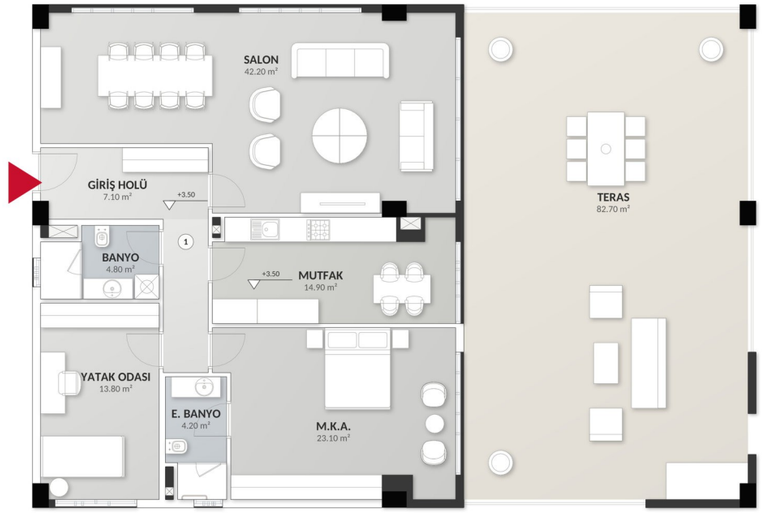

D BLOK · 1. KAT PLANI

KOT +3.50 (170.75)


NET ALAN TOPLAMI : 114.20 m²

AÇIK ALAN (TERAS/BALKON/BAHÇE) : 82.70 m²

BRÜT ALAN : 129.77 m²

No	Mahal	Net alan (m²)
1	KORİDOR	4.10

TOPLAM KAPALI ALAN : 460.02 m²

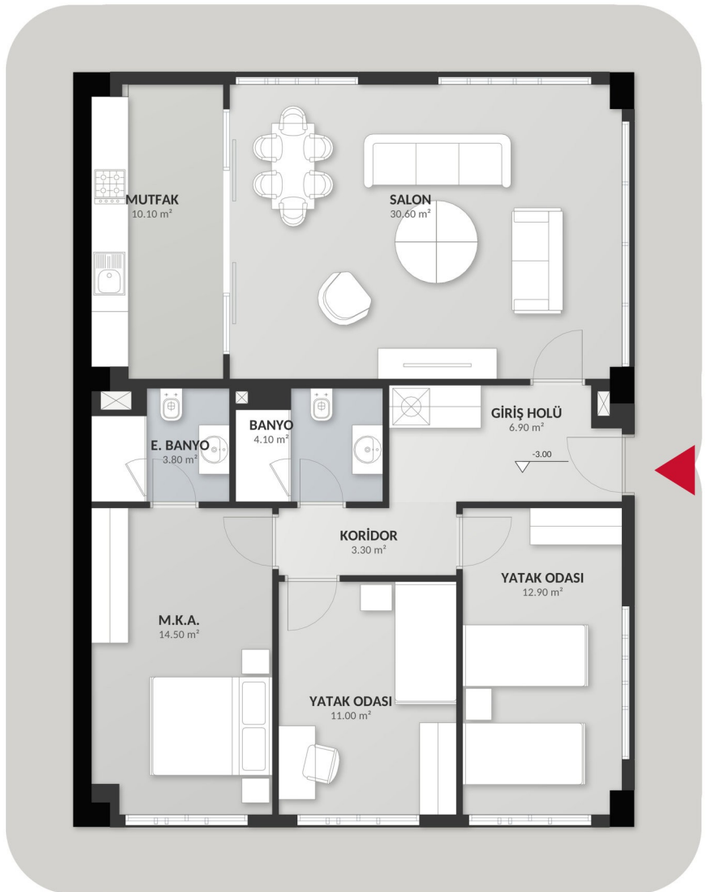

ÖLÇEK 1/100

0 1 2 3 4 5 m

D BLOK · 1. BODRUM KAT PLANI

KOT -3.00 (164.25)

NET ALAN TOPLAMI : 97.20 m²

BRÜT ALAN : 112.54 m²



ÖLÇEK 1/100

0 1 2 3 4 5 m

D BLOK · ZEMİN KAT PLANI

KOT ±0.00 (167.25)

NET ALAN TOPLAMI : 191.40 m²

BRÜT ALAN : 217.71 m²



ÖLÇEK 1/100

0 1 2 3 4 5 m

D BLOK · 1. KAT PLANI

KOT +3.50 (170.75)

NET ALAN TOPLAMI : 114.20 m²

AÇIK ALAN (TERAS/BALKON/BAHÇE) : 82.70 m²

BRÜT ALAN : 129.77 m²

BLOK	KAT	KOT (MUTLAK)	NET ALAN (m²)	AÇIK ALAN (m²)	BRÜT ALAN (m²)
A	1. BODRUM KAT	-2.80 (170.15)	327.40	-	362.00
A	ZEMİN KAT	+1.20 (174.15)	150.40	190.00	170.00
A	1. KAT	+4.70 (177.65)	122.80	25.00	145.04
	A BLOK TOPLAM KAPALI ALAN		**600.60**	**215.00**	**677.04**
B	2. BODRUM KAT	-7.00 (167.15)	376.00	-	409.00
B	1. BODRUM KAT	-4.00 (170.15)	258.50	-	301.68
B	ZEMİN KAT	±0.00 (174.15)	217.20	-	243.44
	B BLOK TOPLAM KAPALI ALAN		**851.70**	**-**	**954.12**
C	1. BODRUM KAT	-4.00 (170.36)	117.80	-	135.00
C	ZEMİN KAT	±0.00 (174.36)	107.10	13.60	135.00
	C BLOK TOPLAM KAPALI ALAN		**224.90**	**13.60**	**270.00**
D	1. BODRUM KAT	-3.00 (164.25)	97.20	-	112.54
D	ZEMİN KAT	±0.00 (167.25)	191.40	-	217.71
D	1. KAT	+3.50 (170.75)	114.20	82.70	129.77
	D BLOK TOPLAM KAPALI ALAN		**402.80**	**82.70**	**460.02**
	GENEL TOPLAM		**2080.00**	**311.30**	**2361.18**

ÖZET

ZEMİN ALTI KAPALI ALAN (BODRUMLAR) : **1320.22 m²**

ZEMİN ÜSTÜ KAPALI ALAN : **1040.96 m²**

TOPLAM KAPALI ALAN : 2361.18 m²

AÇIK ALAN (TERAS / BALKON / KAT BAHÇESİ) : **311.30 m²**

NOTLAR

Brüt alan: terassız kapalı kat alanı, dıştan dışa (kat planı paftalarıyla aynı).

Teras, balkon ve kat bahçesi AÇIK ALAN sütununda ayrı gösterilmiştir.

A 1. kat brüt alanı: kat brütü 170.00 − kat bahçesi 24.96 = 145.04 m².


D 1. kat brüt alanı DXF kat şemasından (129.77 m²); 82.70 m² teras ayrıdır.

Kaynak: 03-boyama/kaynak/era01_ozet.json (PAFTA).

İmar hesapları (emsal, TAKS/KAKS, arsa alanı): [DOLDURULACAK]

ATMOSFER ESKİZİ (KARAKALEM)

IFC tarafından eklenecek (tam sayfa, 420 × 297 mm)

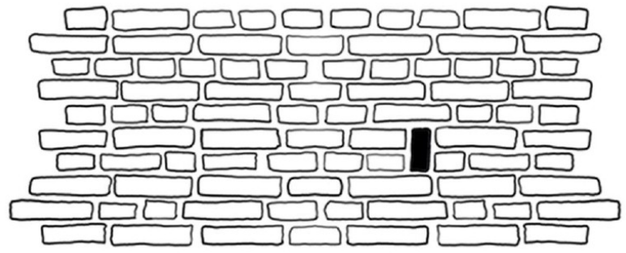

IFC Architects

İLETİŞİM
Adres: Burhaniye Mah. Bahçeler Sk. No:4, 34676
Üsküdar/İstanbul
t: (0216) 362 17 02
f: (0216) 362 17 03
www.ifcmimarlik.com