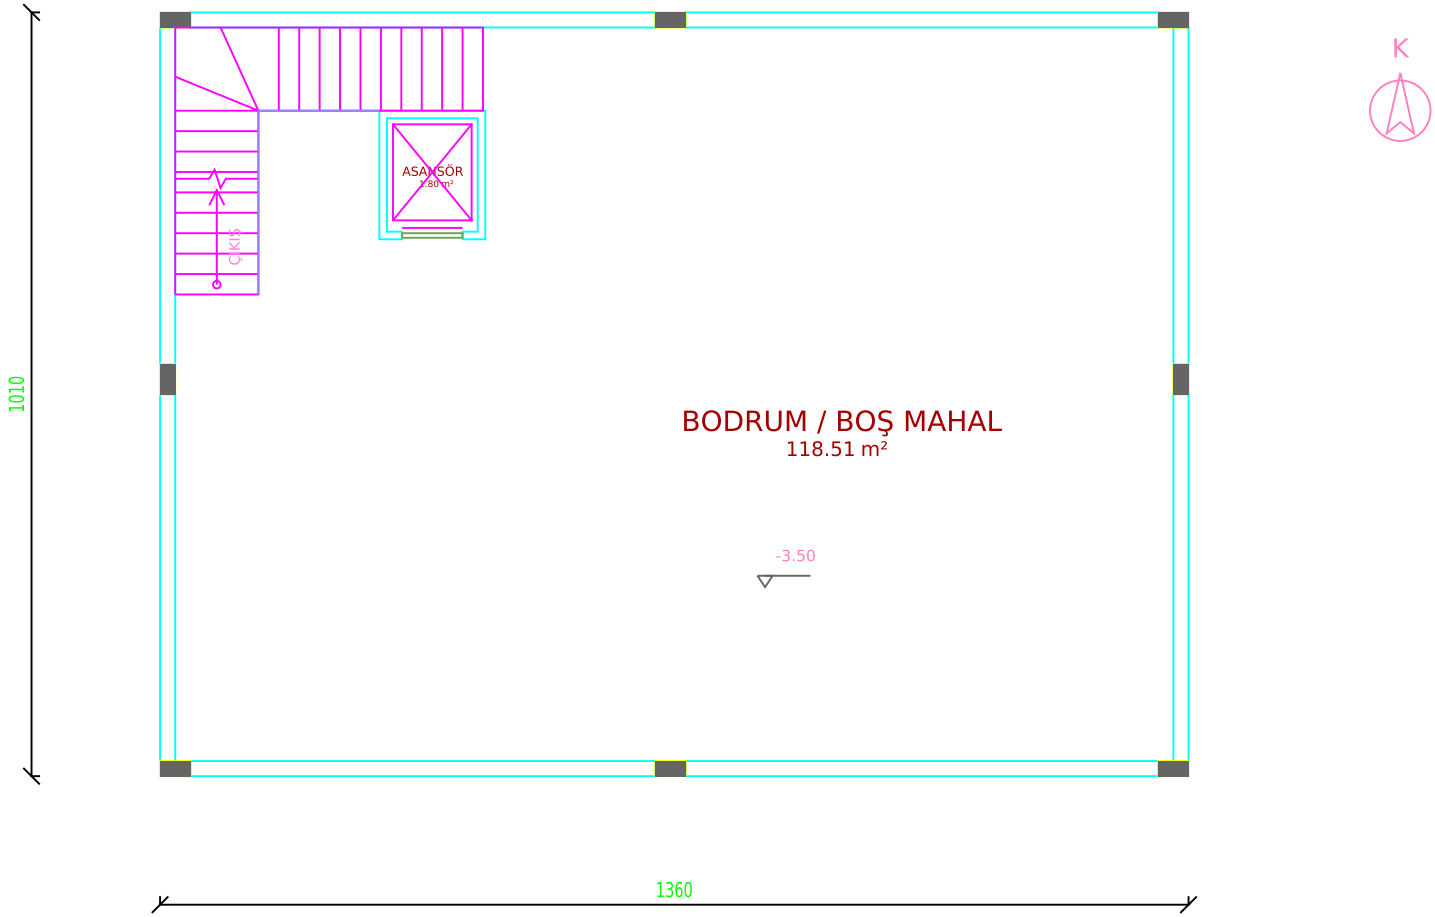


K

BODRUM KAT


KOT -3.50 KAT BRÜT ALANI 137.36 m²

IFC Architects

PROJE	Deneme Villa
PROJE KODU	DNM01
ÇİZİM	**BODRUM KAT PLANI**
ÖLÇEK	1/100
KAĞIT	A4
TARİH	11.11.2026
SÜRÜM	v02
AŞAMA	KONSEPT
DURUM	**TASLAK - onay bekliyor**
KOT	-3.50 m
BRÜT ALAN	137.36 m²
PAFTA	1/5

0 1 2 3 4 5 m

IFC Architects | çizim birimi cm, kotlar m

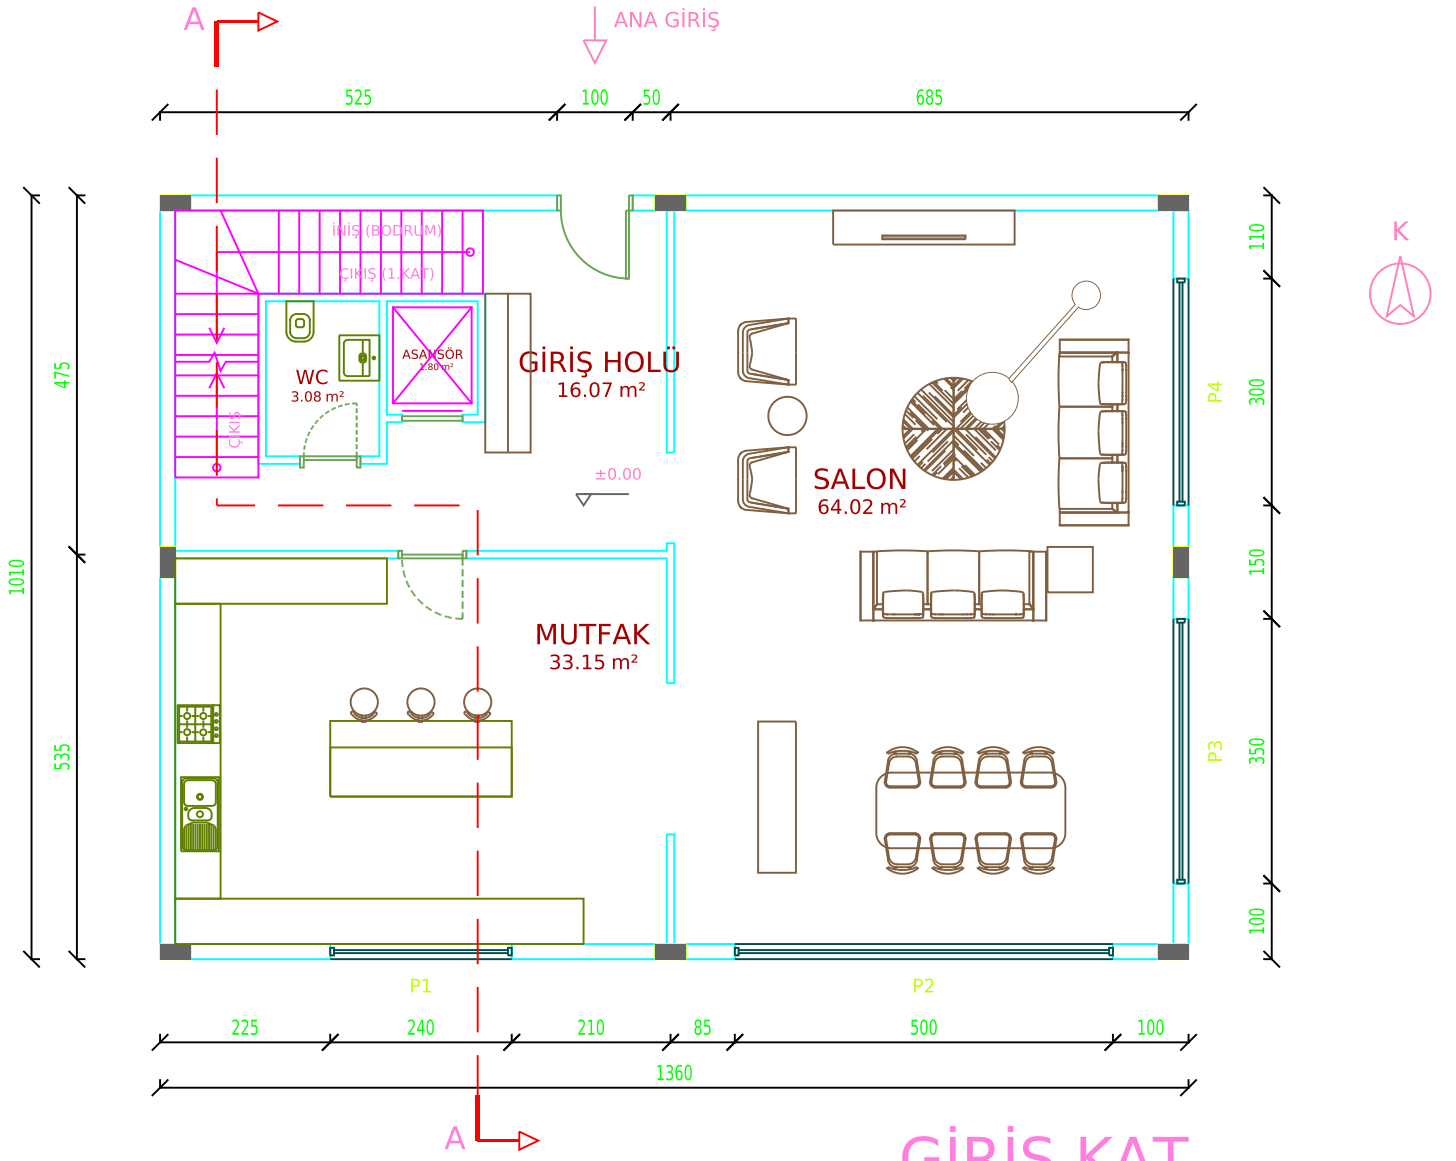

GİRİŞ KAT

KOT ±0.00 KAT BRÜT ALANI 137.36 m²


K

IFC Architects

PROJE	Deneme Villa
PROJE KODU	DNM01
ÇİZİM	**GİRİŞ KAT PLANI**
ÖLÇEK	1/100
KAĞIT	A4
TARİH	11.11.2026
SÜRÜM	v02
AŞAMA	KONSEPT
DURUM	**TASLAK - onay bekliyor**
KOT	±0.00 m
BRÜT ALAN	137.36 m²
PAFTA	2/5

0 1 2 3 4 5 m

IFC Architects | çizim birimi cm, kotlar m

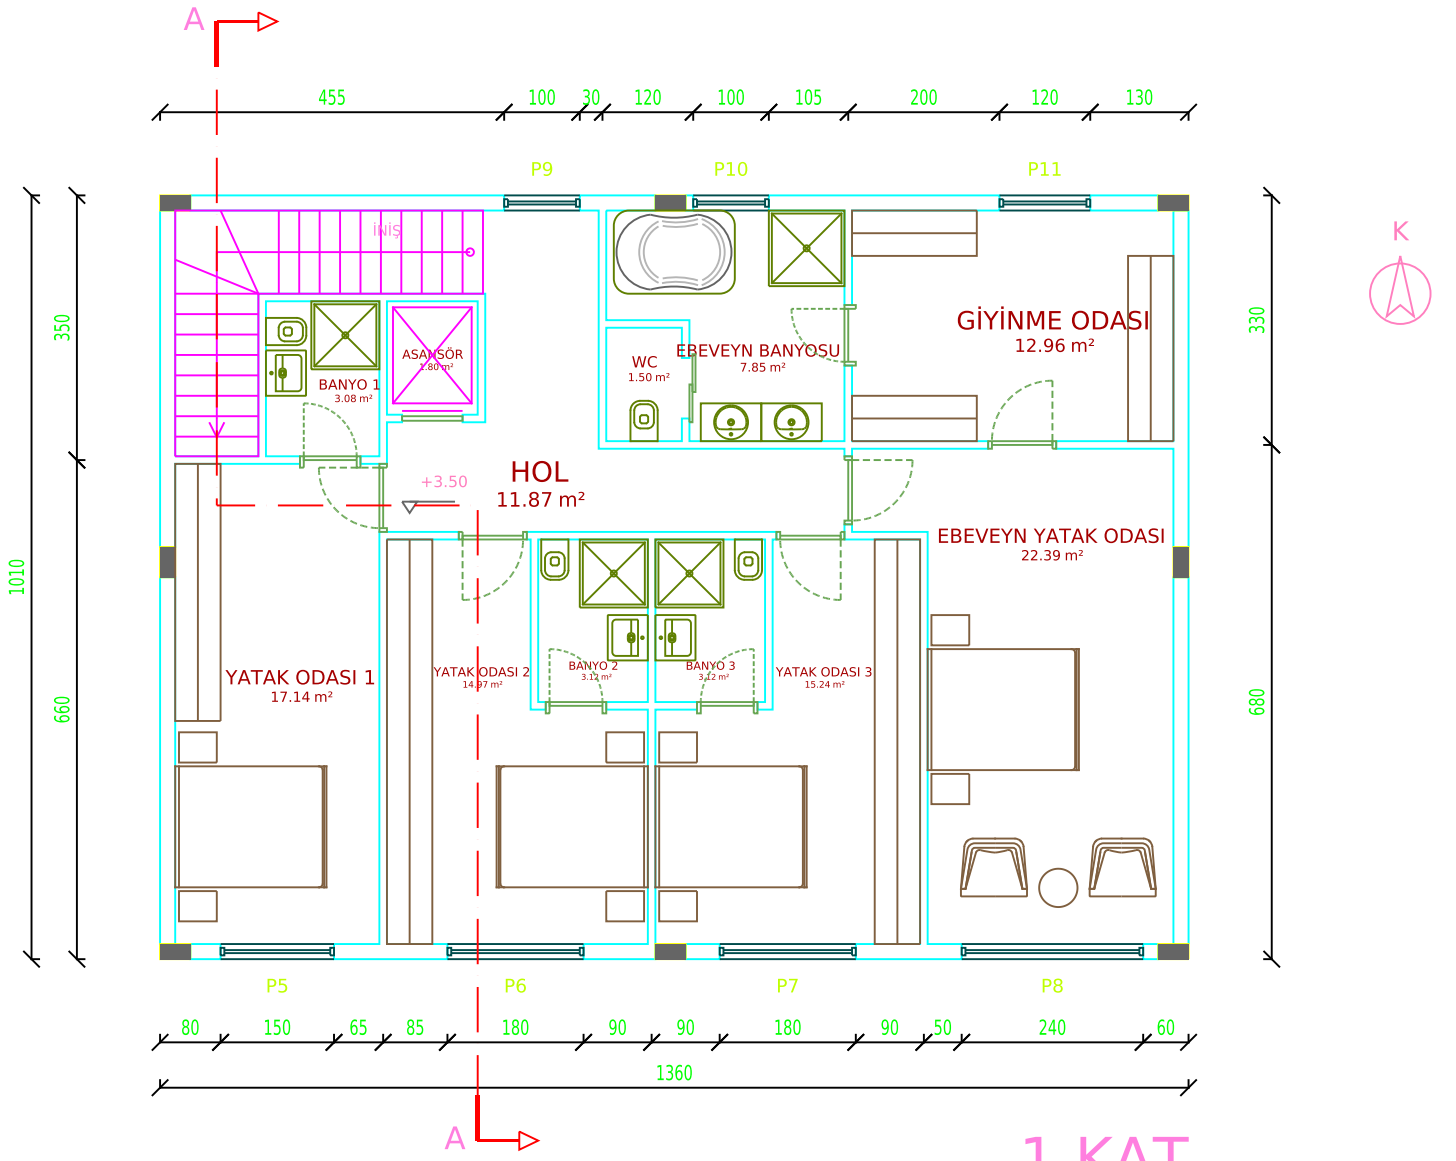

K

1.KAT


KOT +3.50 KAT BRÜT ALANI 137.36 m²

IFC Architects

PROJE	Deneme Villa
PROJE KODU	DNM01
ÇİZİM	**1. KAT PLANI**
ÖLÇEK	1/100
KAĞIT	A4
TARİH	11.11.2026
SÜRÜM	v02
AŞAMA	KONSEPT
DURUM	**TASLAK - onay bekliyor**
KOT	+3.50 m
BRÜT ALAN	137.36 m²
PAFTA	3/5

0 1 2 3 4 5 m

IFC Architects | çizim birimi cm, kotlar m

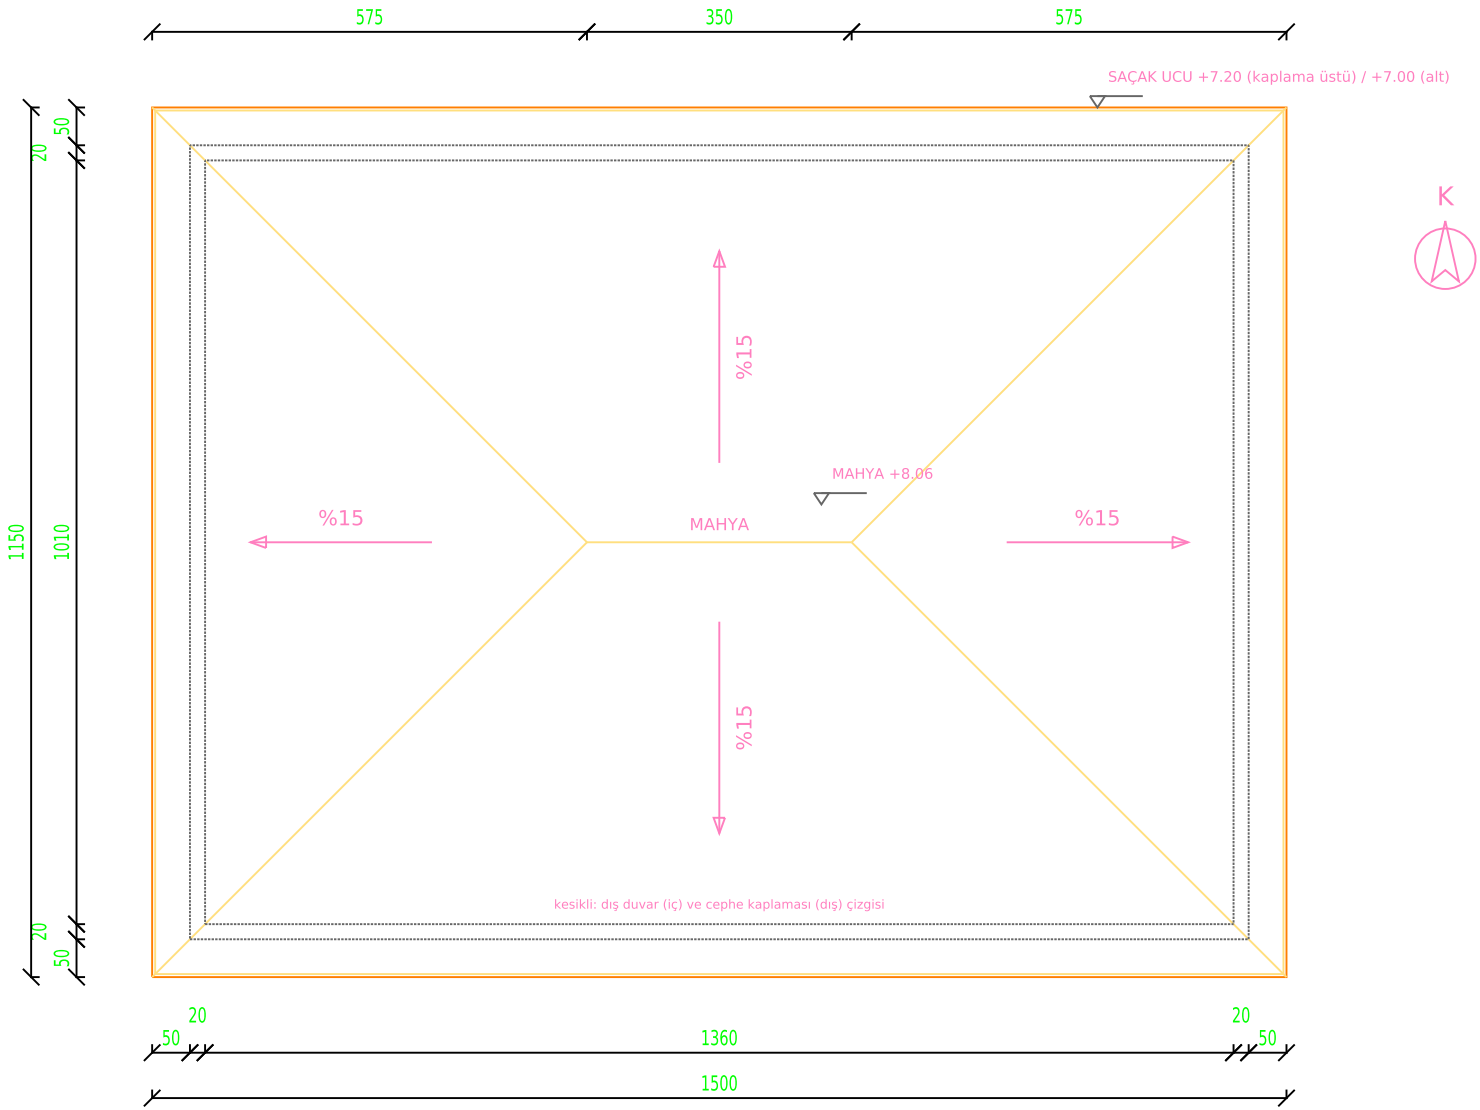

K

METAL KENET ÇATI KAPLAMASI
4 YÖNE KIRMA ÇATI, EĞİM %15
SAÇAK 50 cm (cephe kaplaması dış yüzünden)
ÇATI ARASI MAHAL OLARAK KULLANILMAZ

ÇATI PLANI


SAÇAK +7.20 MAHYA +8.06 ÇATI İZDÜŞÜM ALANI 172.50 m²

IFC Architects

PROJE	Deneme Villa
PROJE KODU	DNM01
ÇİZİM	**ÇATI PLANI**
ÖLÇEK	1/100
KAĞIT	A4
TARİH	11.11.2026
SÜRÜM	v02
AŞAMA	KONSEPT
DURUM	**TASLAK - onay bekliyor**
MAHYA	+8.06 m
SAÇAK UCU	+7.20 m
PAFTA	4/5

0 1 2 3 4 5 m

IFC Architects | çizim birimi cm, kotlar m

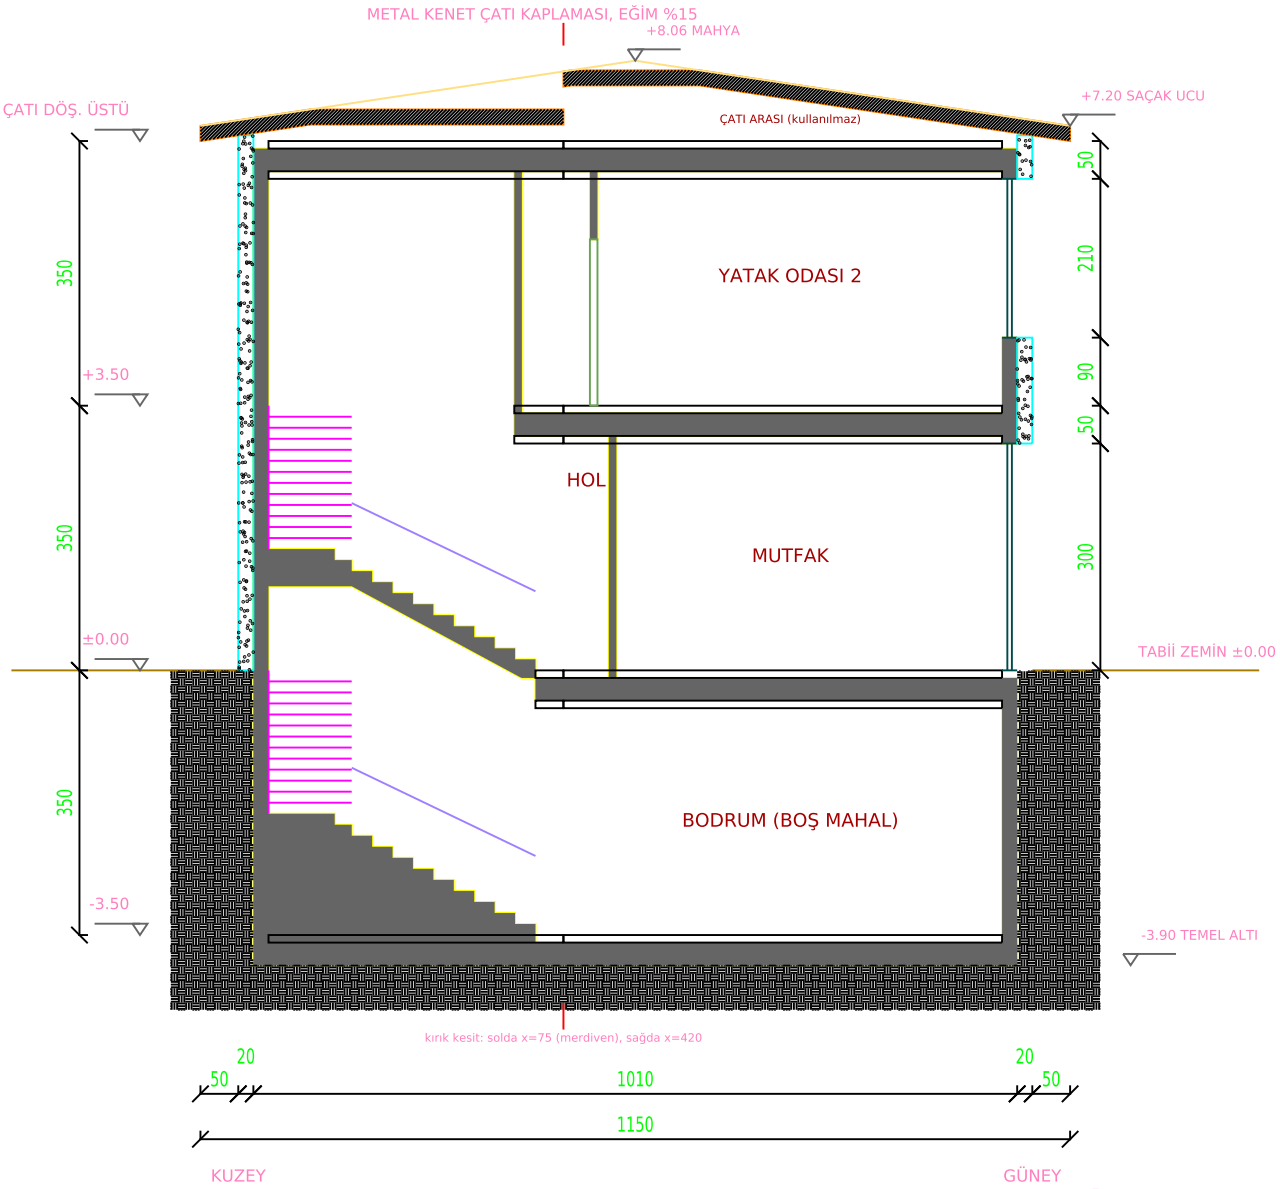

KESİT A-A

1/100 · bakış doğuya (kuzey solda) · kesit hattı giriş kat ve 1. kat planlarında
Döşeme paketi 50 (kaplama 10 + taşıyıcı 30 + tavan 10) · dış duvar 20 + cephe kaplaması 20 · pencere yükseklikleri VARSAYIM

IFC Architects

PROJE	Deneme Villa
PROJE KODU	DNM01
ÇİZİM	**KESİT A-A**
ÖLÇEK	1/100
KAĞIT	A4
TARİH	11.11.2026
SÜRÜM	v02
AŞAMA	KONSEPT
DURUM	**TASLAK - onay bekliyor**
KAT YÜKS.	3.50 m
MAHYA	+8.06 m
PAFTA	5/5

0 1 2 3 4 5 m

IFC Architects | çizim birimi cm, kotlar m